## GENERAL NOTES


1. ALL DIMENSIONS IN MM
2. VERIFY ON SITE
3. FIRE RATED DOORS: FD30

REVISION C




LEVEL 2 PLAN

| CONVERTIFY ARCHITECTS | |
|---|---|
| LEVEL 2 FLOOR PLAN | |
| DRAWN BY: J. SMITH | DATE: 2026-03-14 |
| SCALE 1:100 | **SHEET A-201** |

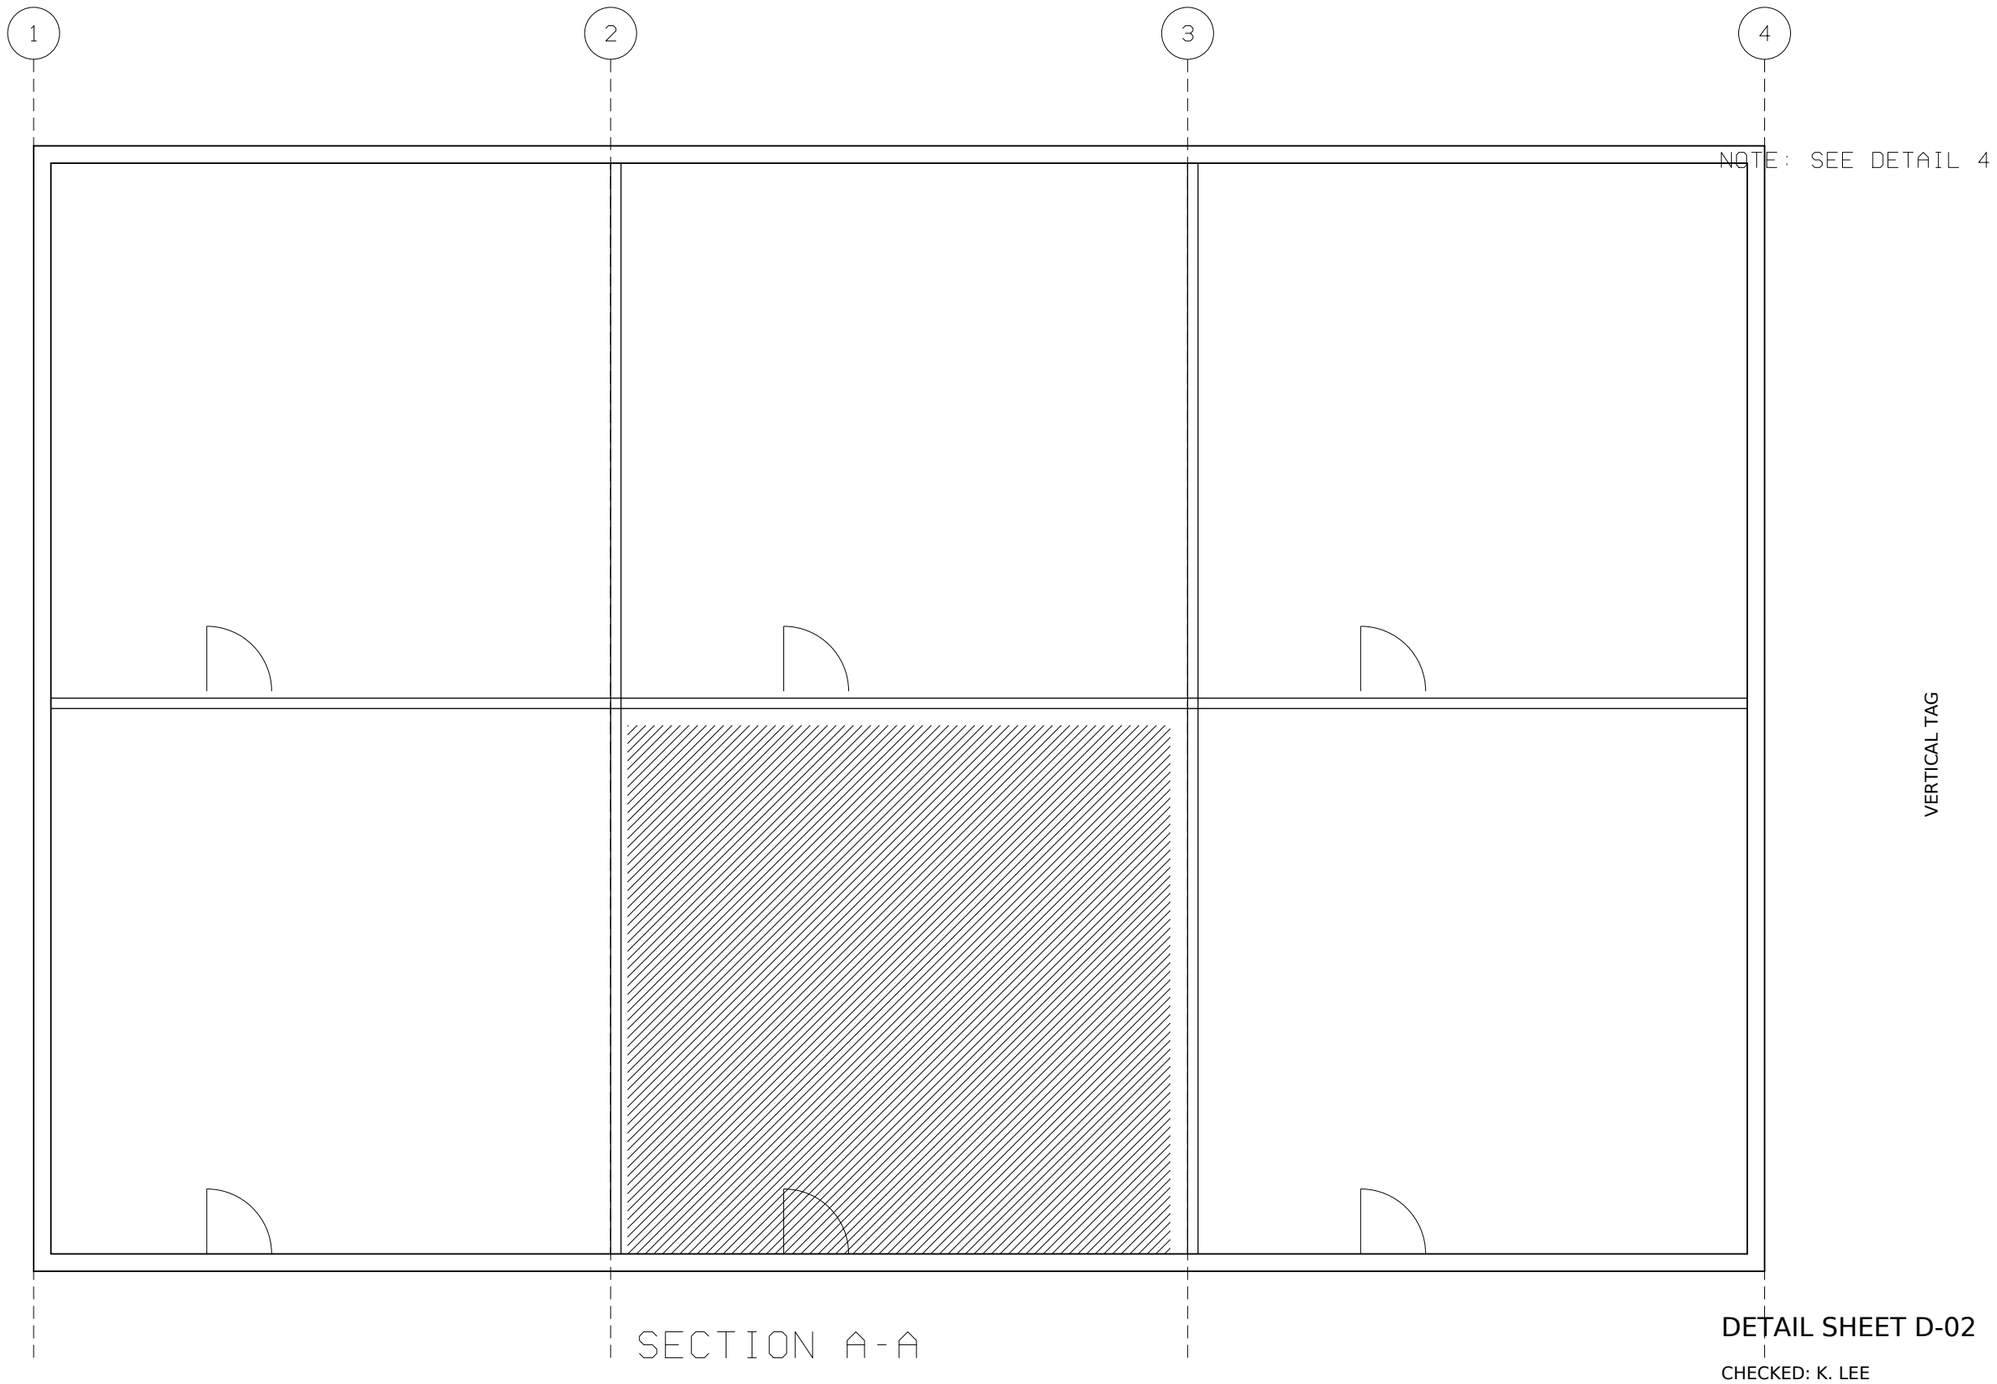



VERTICAL TAG

SECTION A-A

DETAIL SHEET D-02


CHECKED: K. LEE

# SITE PLAN

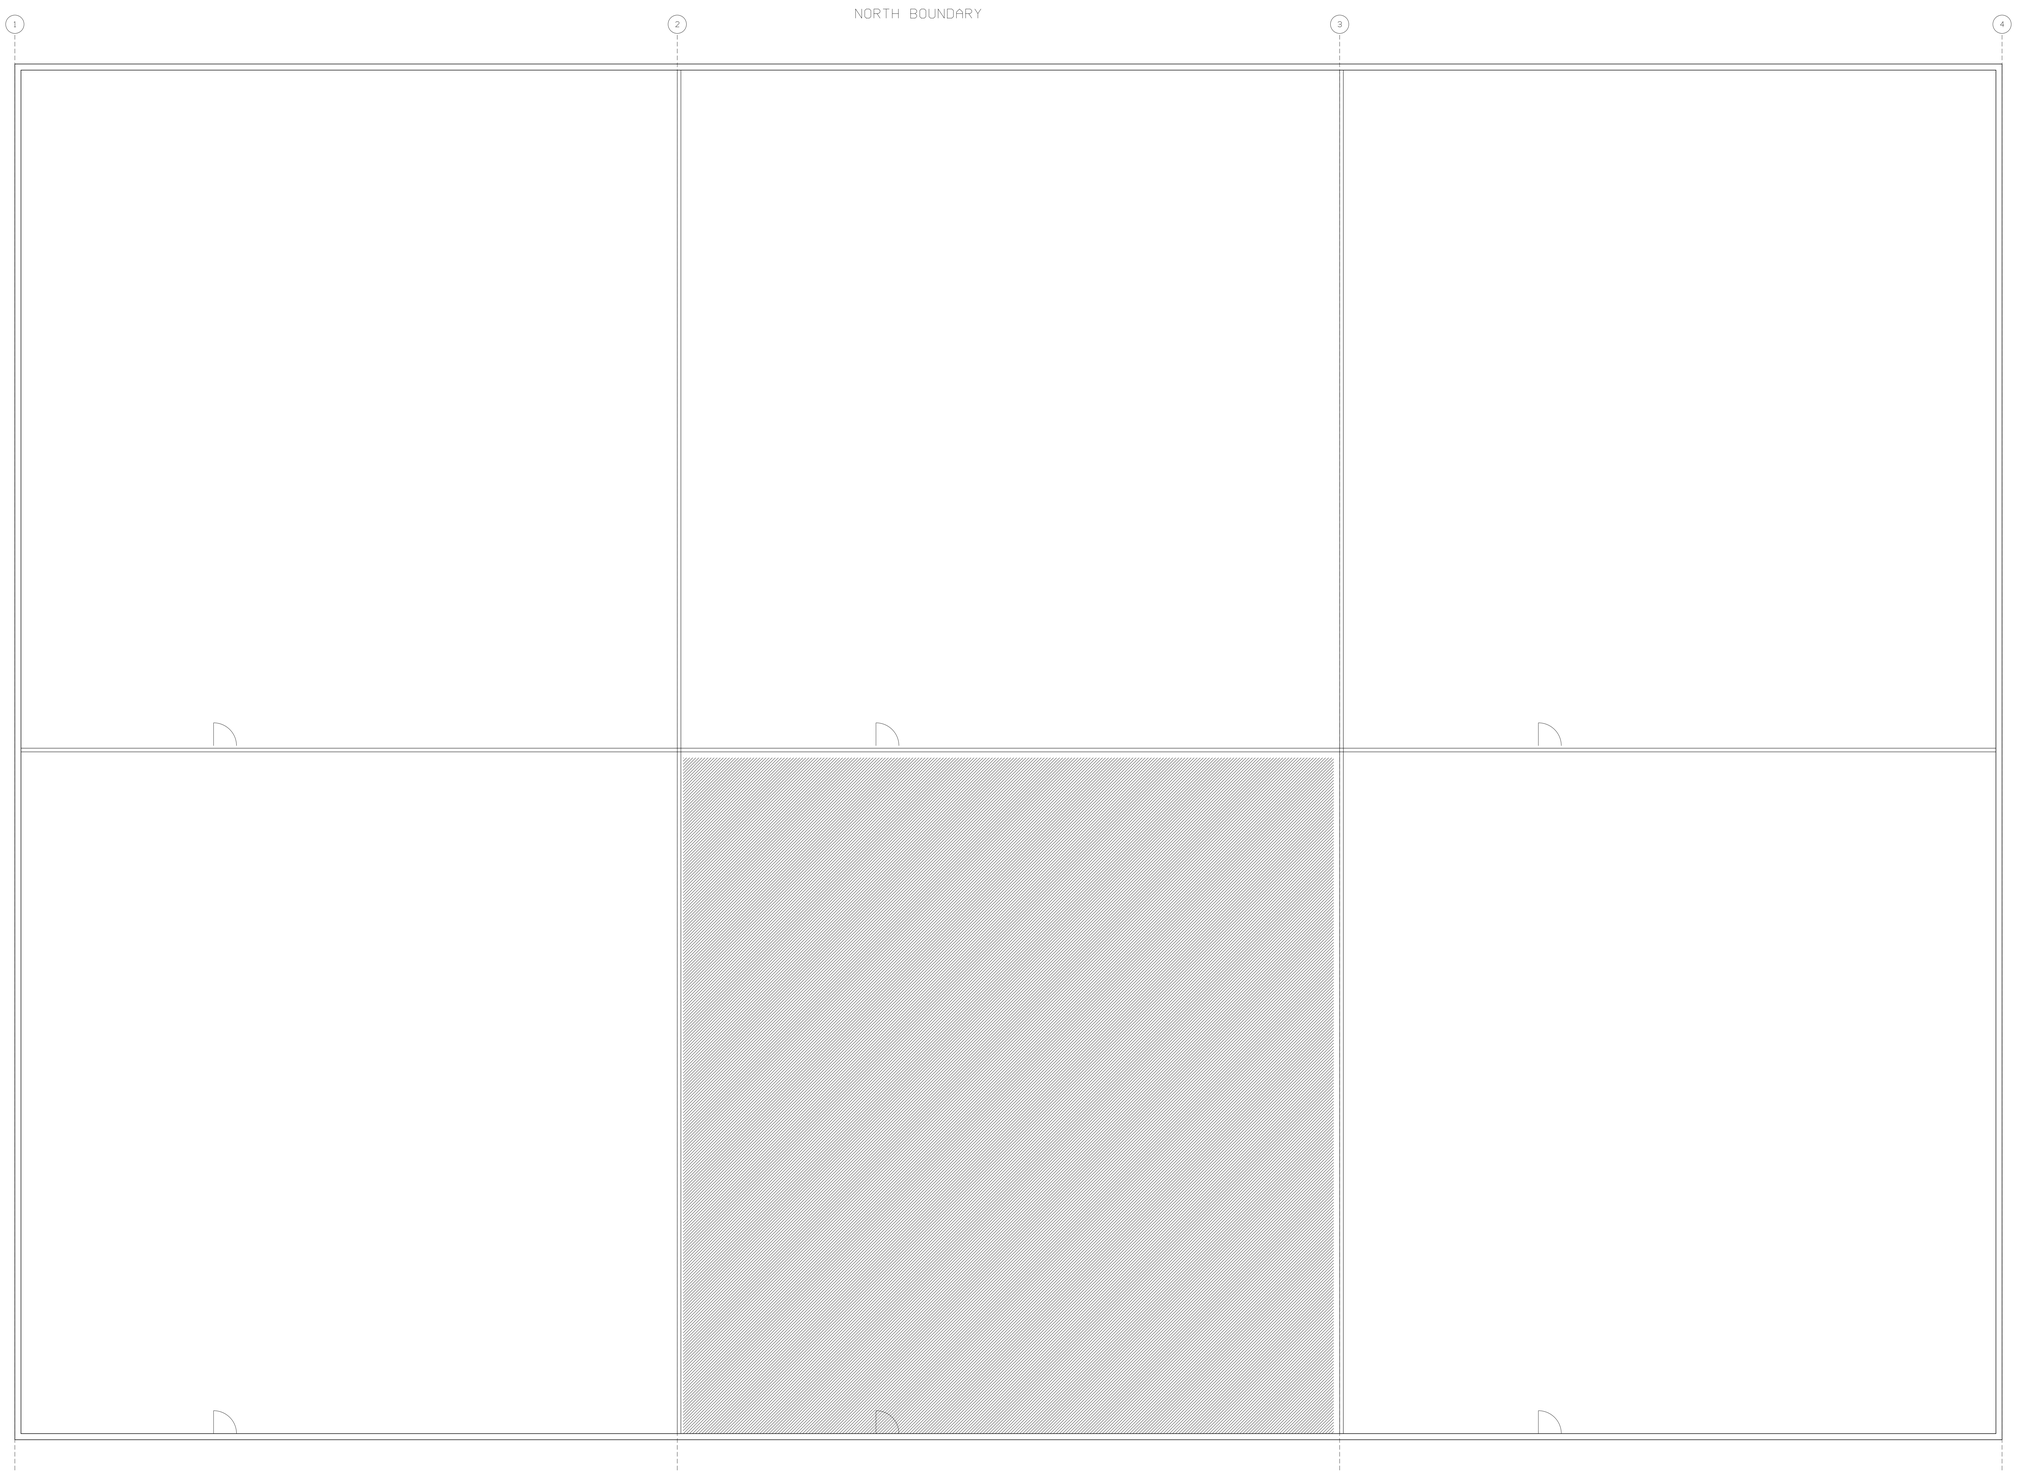


A0 MASTER SHEET

SHX ONLY SHEET

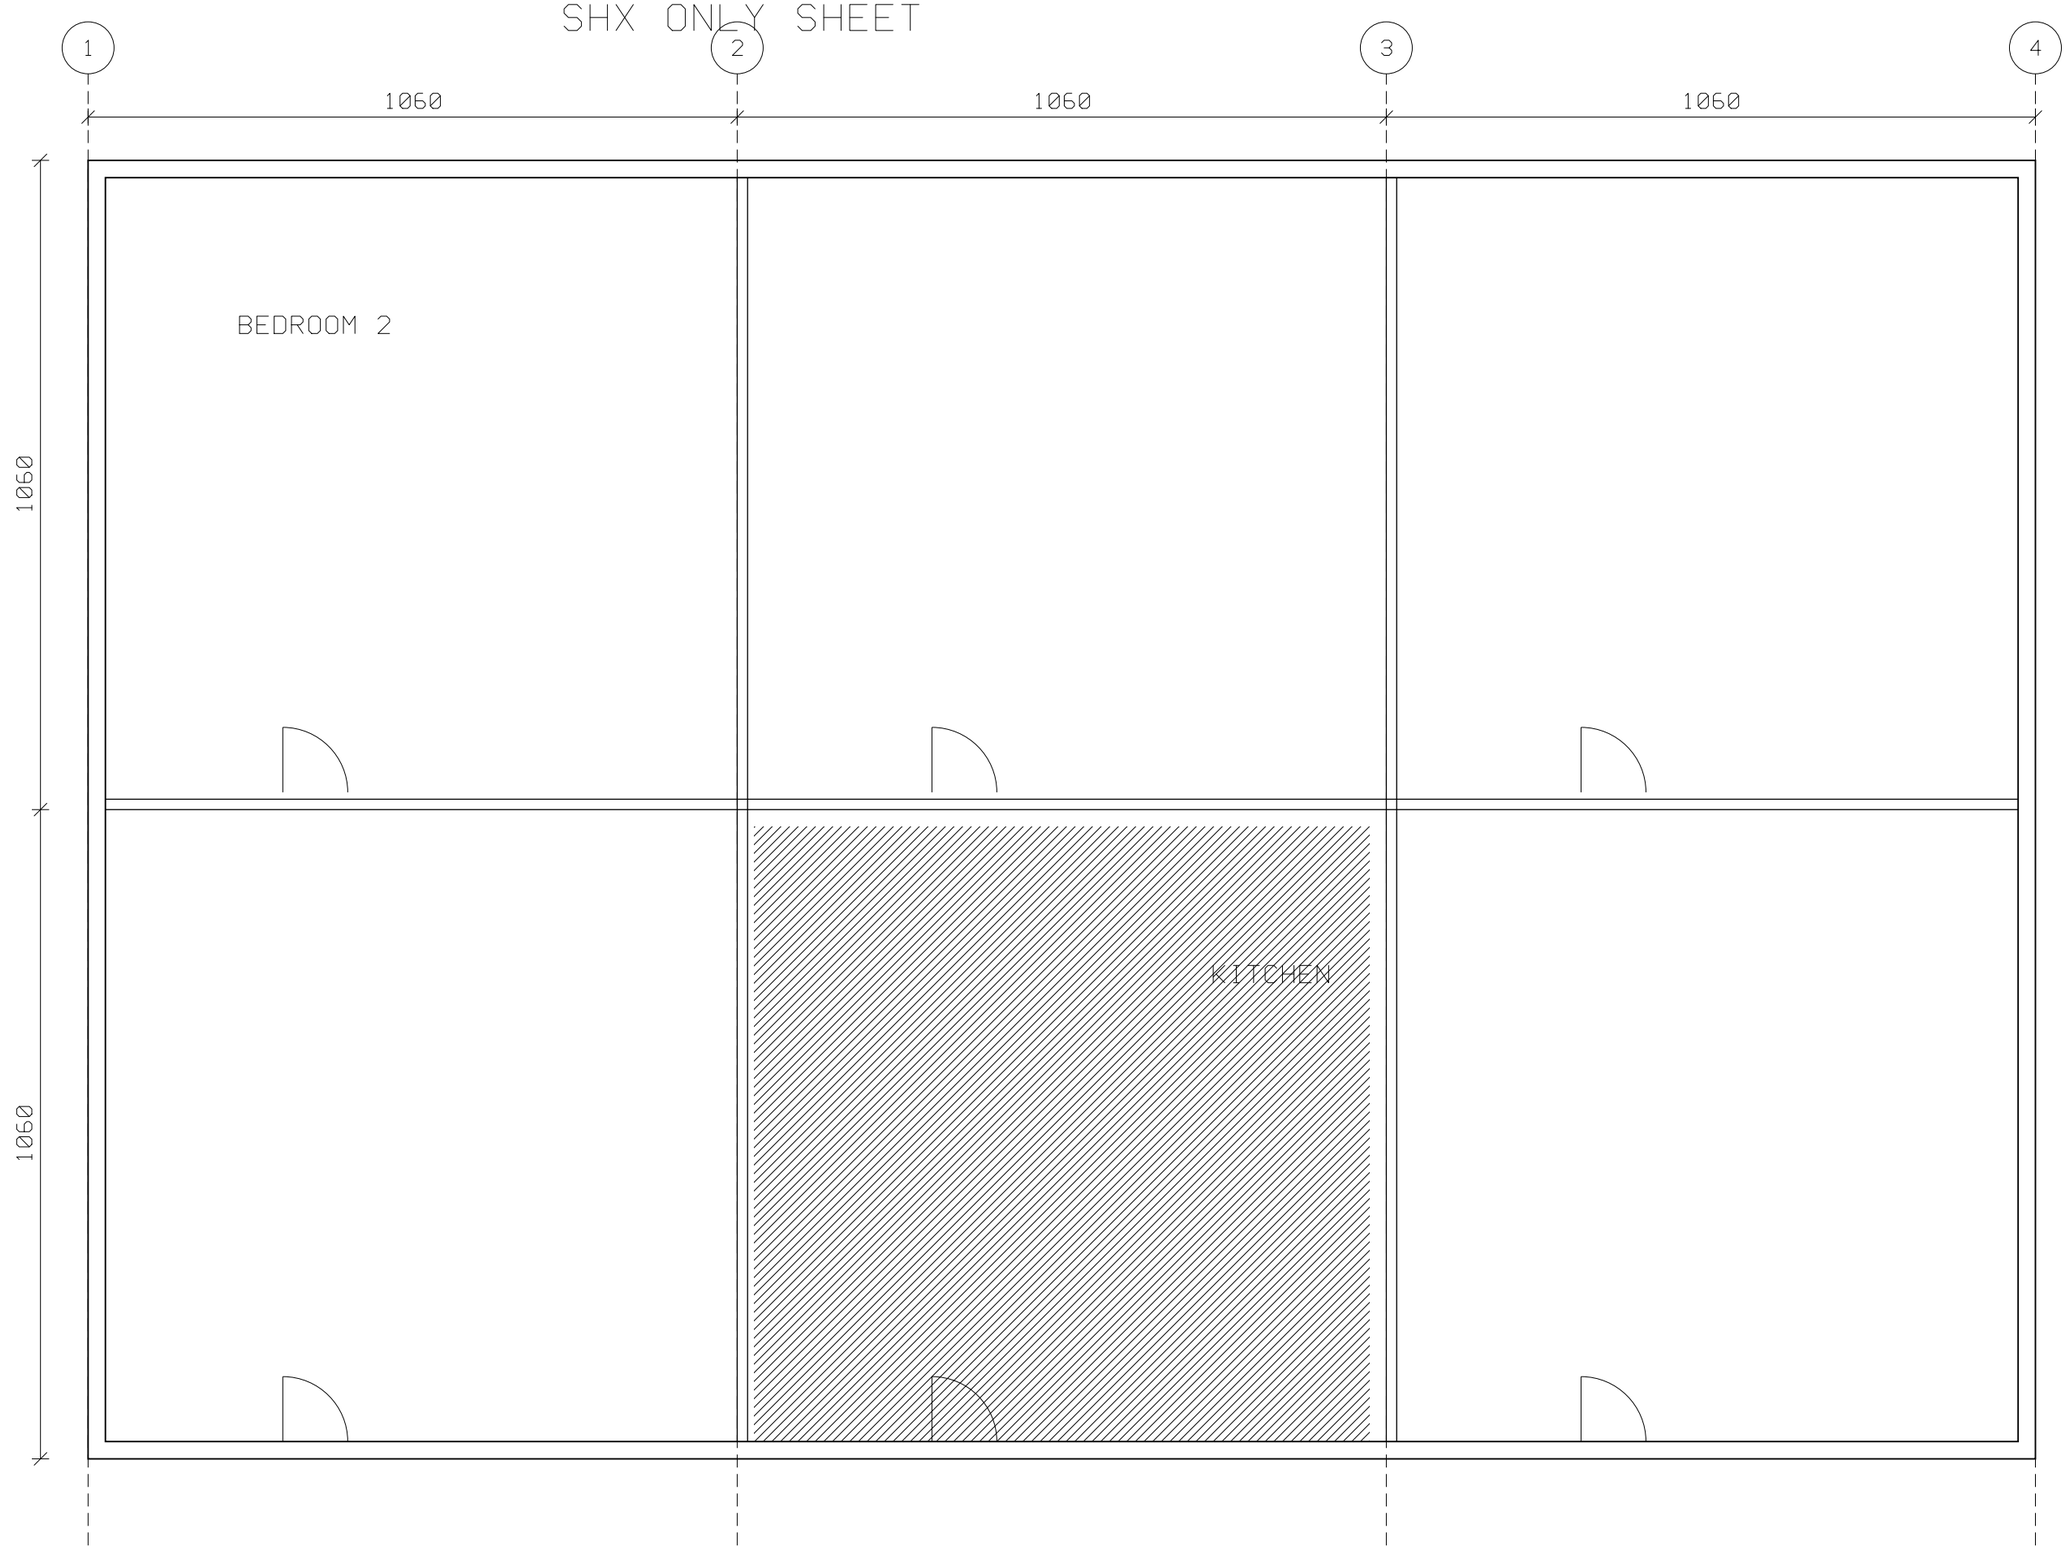

# DETAIL 4 - WALL BASE



# DRAWING SET - ISSUE 3

PROJECT 2026-114

FOR TENDER